



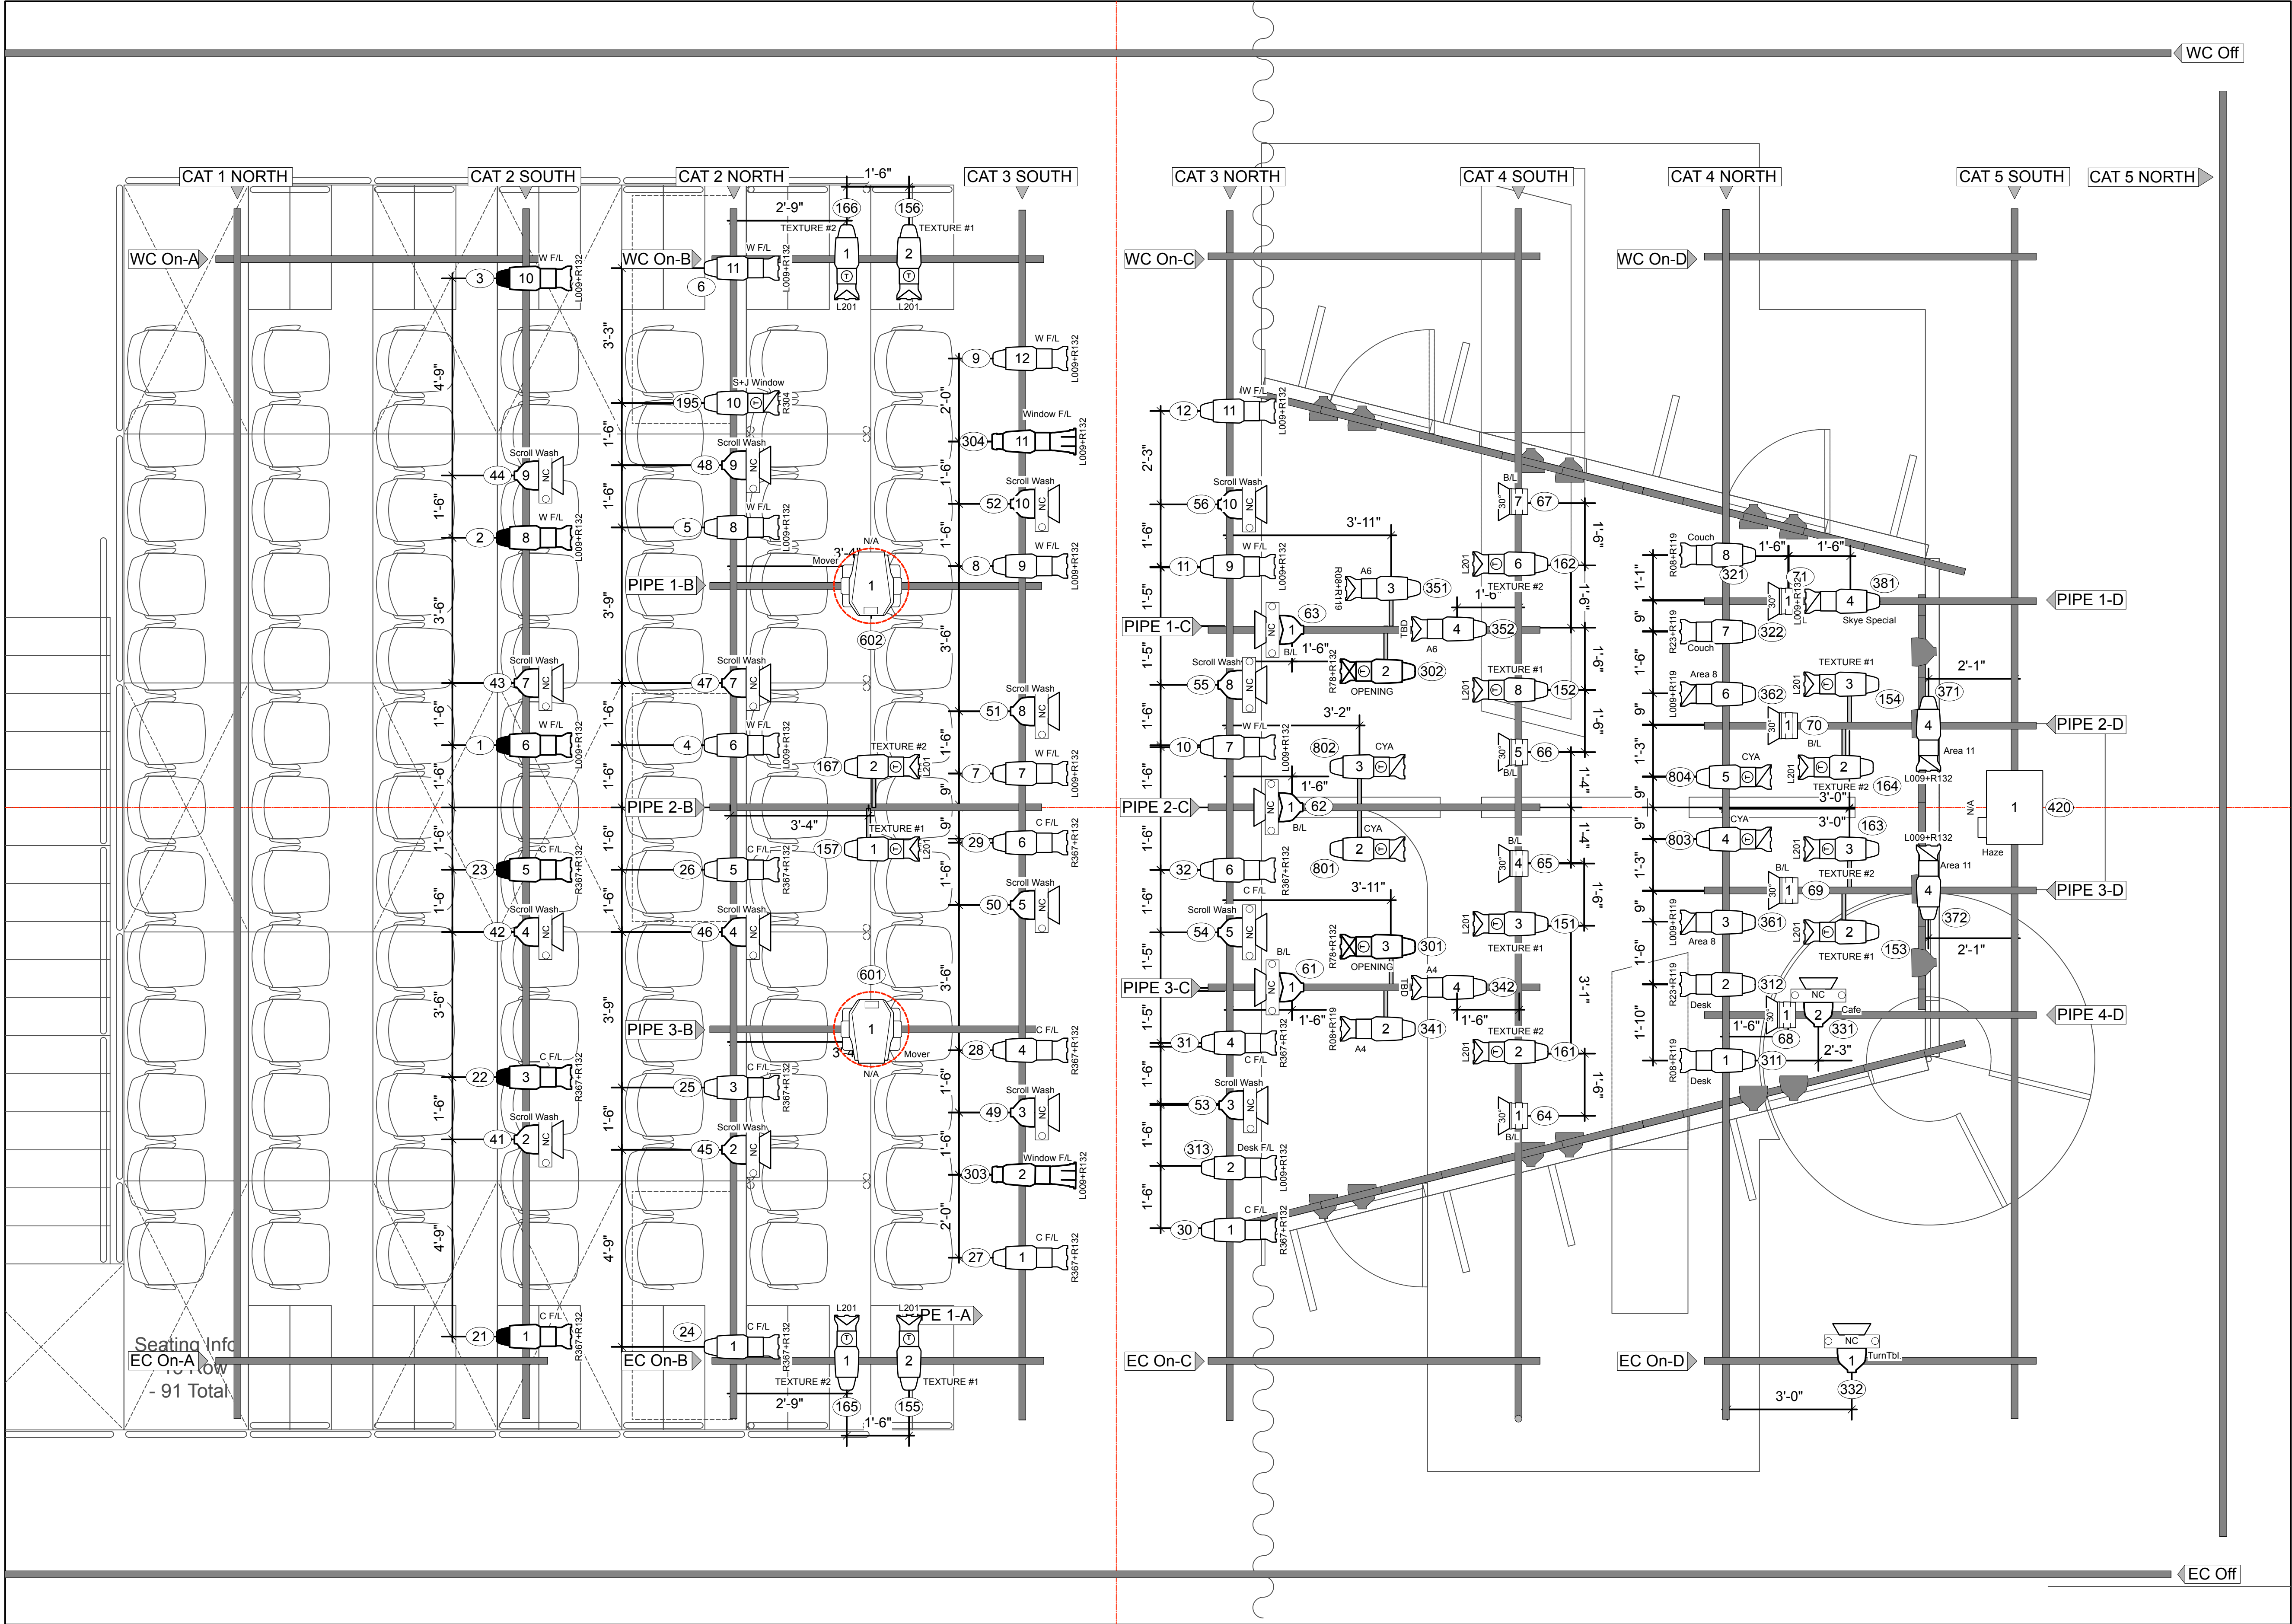

Symbol Key:

- ETC Source 4 14deg @575 W
- ETC Source 4 19deg @575 W
- ETC Source 4 26deg @575 W
- ETC Source 4 36deg @575 W
- ETC Source 4 50deg @575 W
- ETC Source 4 PAR MFL @575 W
- ETC Source 4 PAR WFL @575 W
- Hazebase Base Hazer Pro @1500 W
- Elation Level Q7 @127
- ETC Paletta 42 @432 W
- High End Systems SolaFrame 750 @562 W
- Cuepix Tri @0 W

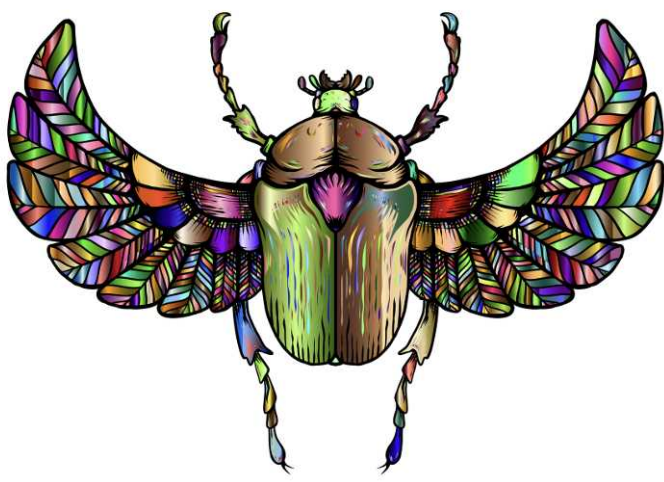

LEFT UNHEARD


HEALY THEATER AT DEPAUL THEATER SCHOOL
2400 N SHEFFIELD AVE CHICAGO, IL

DIRECTOR	DENISE SERNA
SCENIC DESIGNER	IZAAK KARY
LIGHTING DESIGNER	ADRIEN MATHIEU
STAGE MANAGEMENT	TESS DUNCAN
COSTUME DESIGNER	SPENCER HARRIGAN
TECHNICAL DIRECTOR	REID STADELMAN
WAM DESIGNER	CARISSA SETH
SOUND DESIGNER	MIA HOWARD

DATE: 3/30/25 SCALE: 1/4=1'0"


PLATE
1
OF 6

OVERHEAD LIGHT PLOT

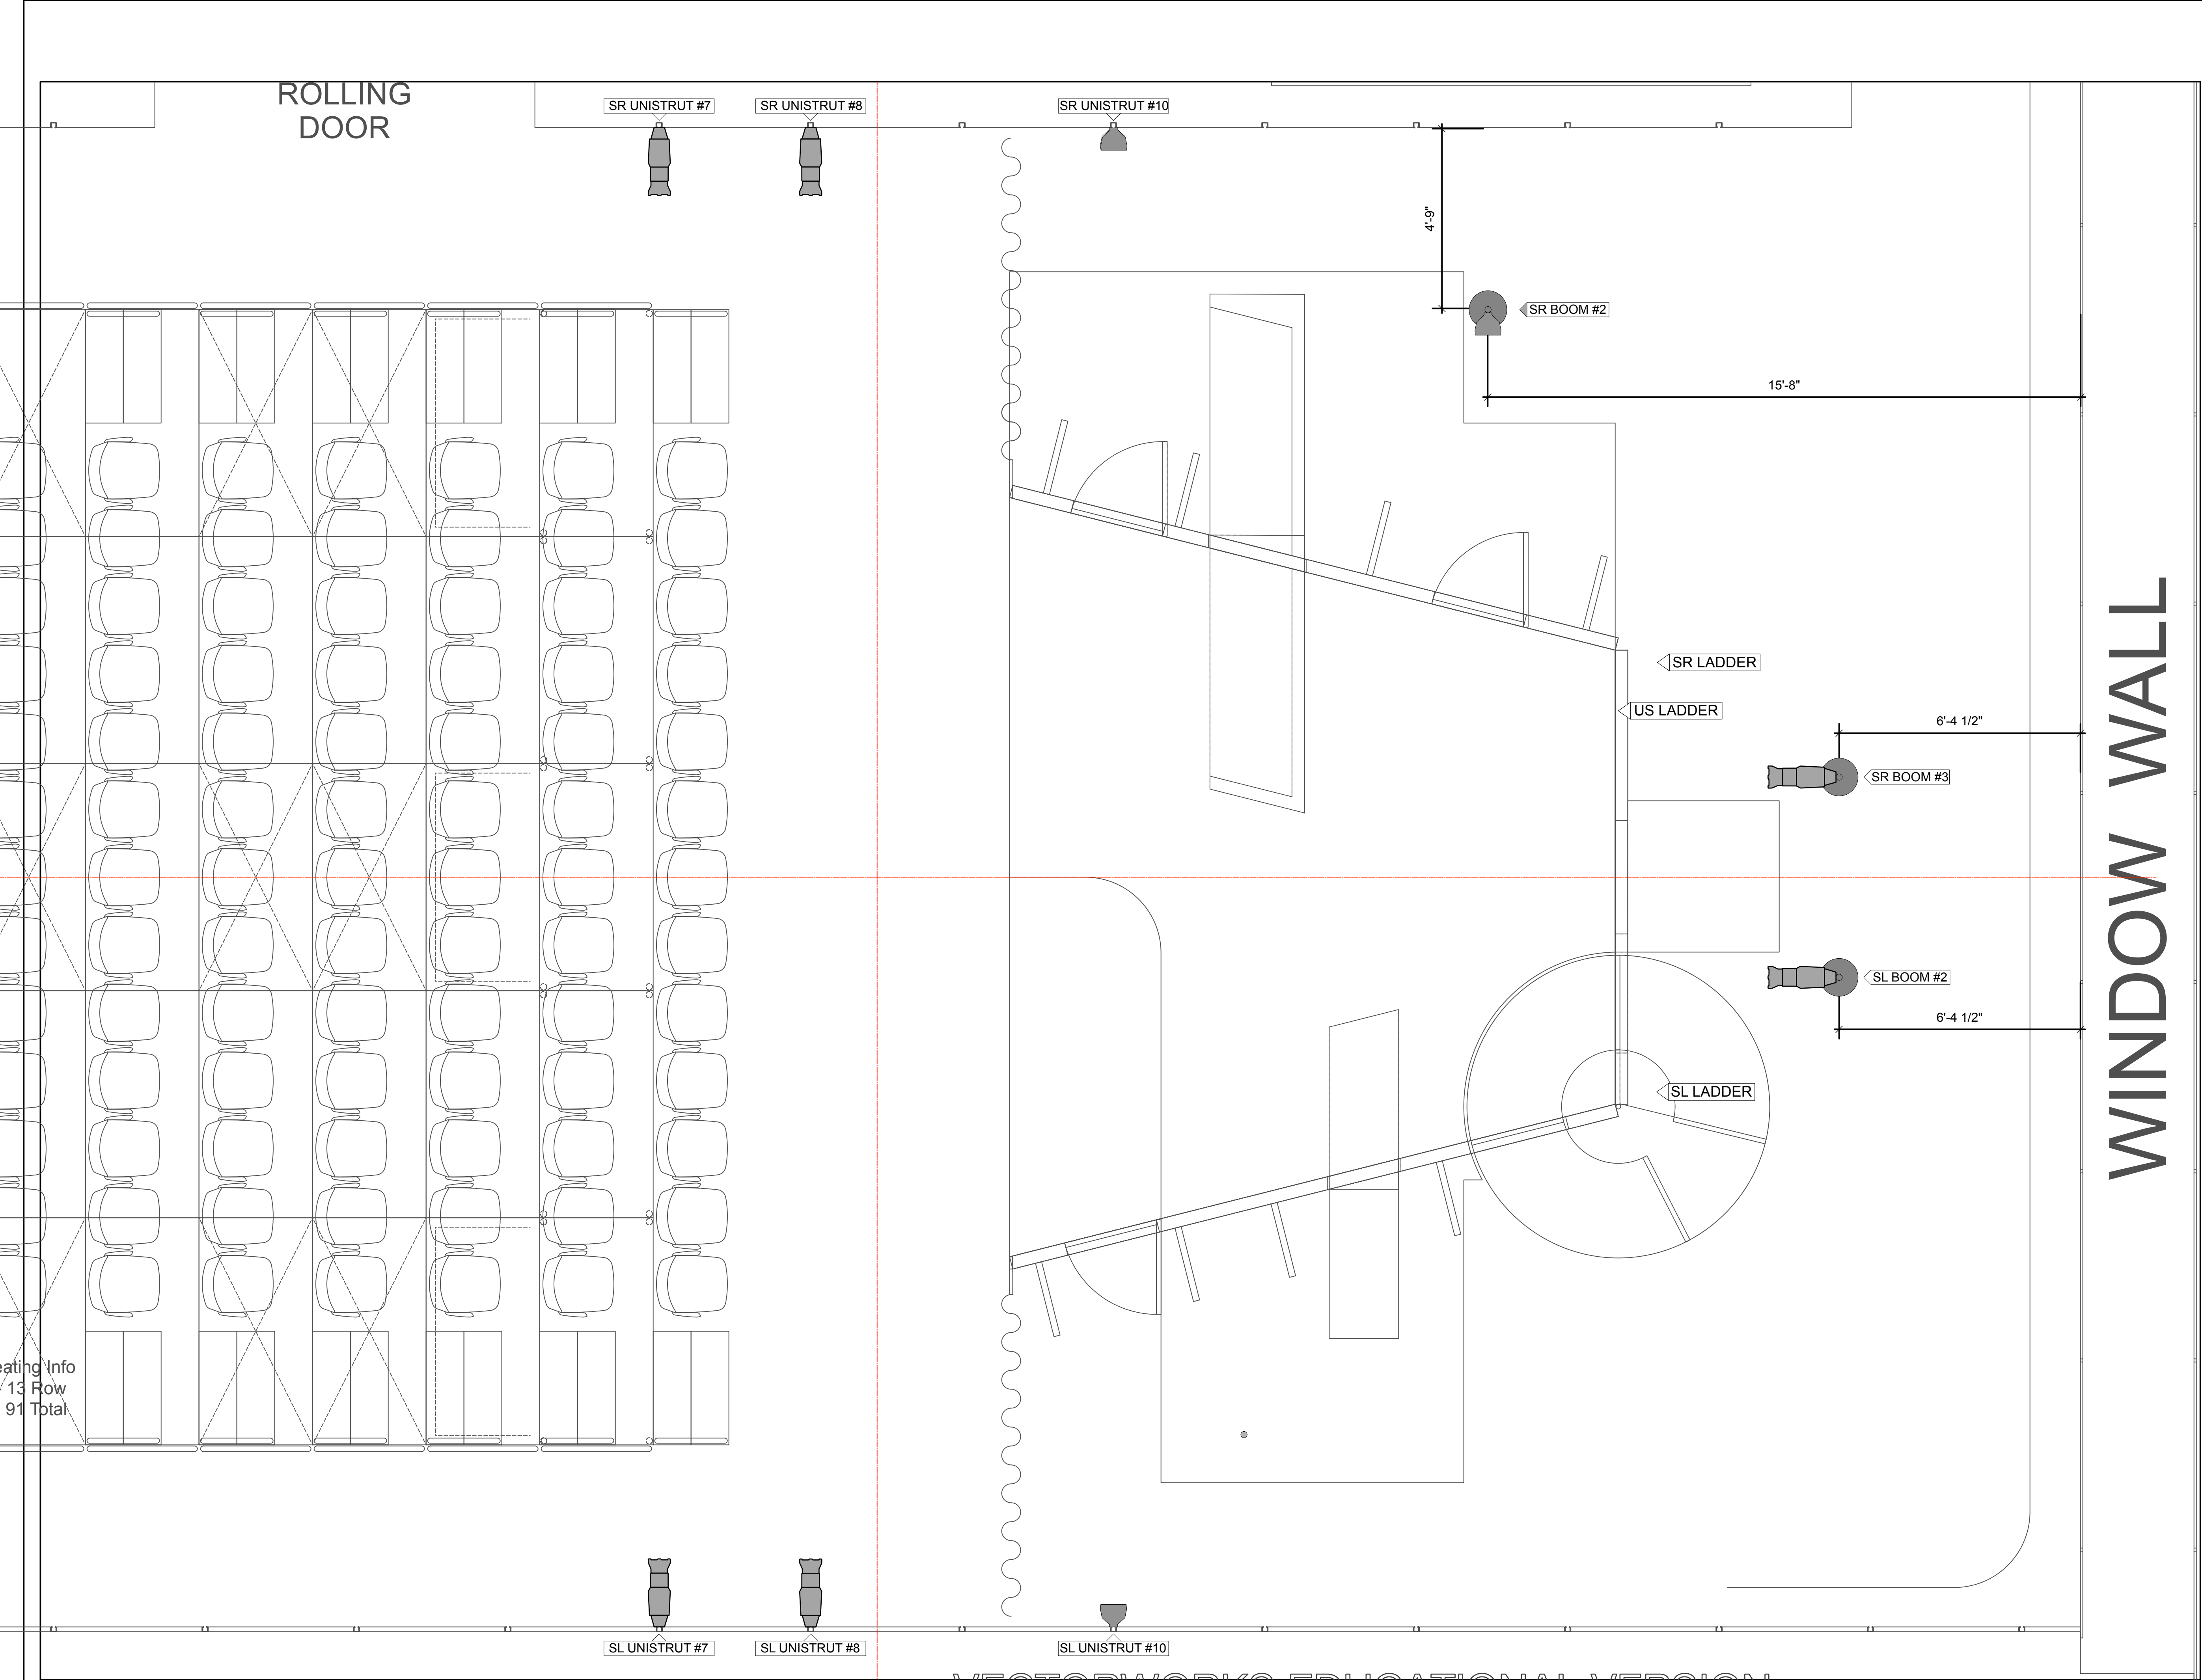

Symbol Key:

	ETC Source 4 14deg @575 W
	ETC Source 4 19deg @575 W
	ETC Source 4 26deg @575 W
	ETC Source 4 36deg @575 W
	ETC Source 4 50deg @575 W
	ETC Source 4 PAR MFL @575 W
	ETC Source 4 PAR WFL @575 W
	Hazebase Base Hazer Pro @1500 W
	Elation Level Q7 @127
	ETC Paletta 42 @432 W
	High End Systems SolaFrame 750 @562 W
	Cuepix Tri @0 W

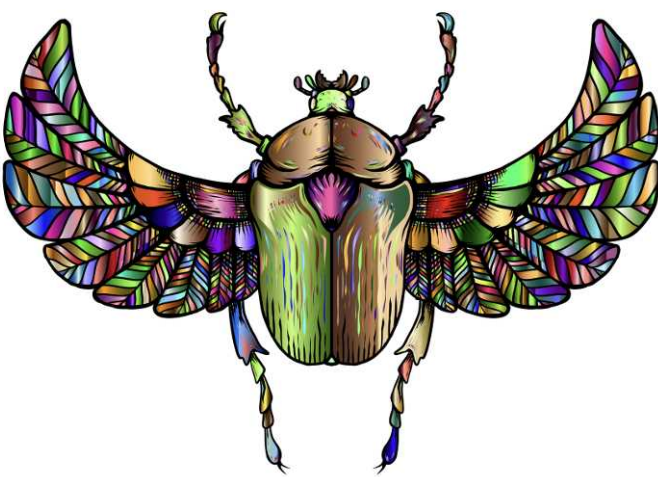

LEFT UNHEARD


HEALY THEATER AT DEPAUL THEATER SCHOOL
2400 N SHEFFIELD AVE CHICAGO, IL

DIRECTOR	DENISE SERNA
SCENIC DESIGNER	IZAAK KARY
LIGHTING DESIGNER	ADRIEN MATHIEU
STAGE MANAGEMENT	TESS DUNCAN
COSTUME DESIGNER	SPENCER HARRIGAN
TECHNICAL DIRECTOR	REID STADELMAN
WAM DESIGNER	CARISSA SETH
SOUND DESIGNER	MIA HOWARD

DATE: 3/30/25 SCALE: 1/4=1'0"


PLATE
2
OF 6

DECK + BOOM DIMENSIONS

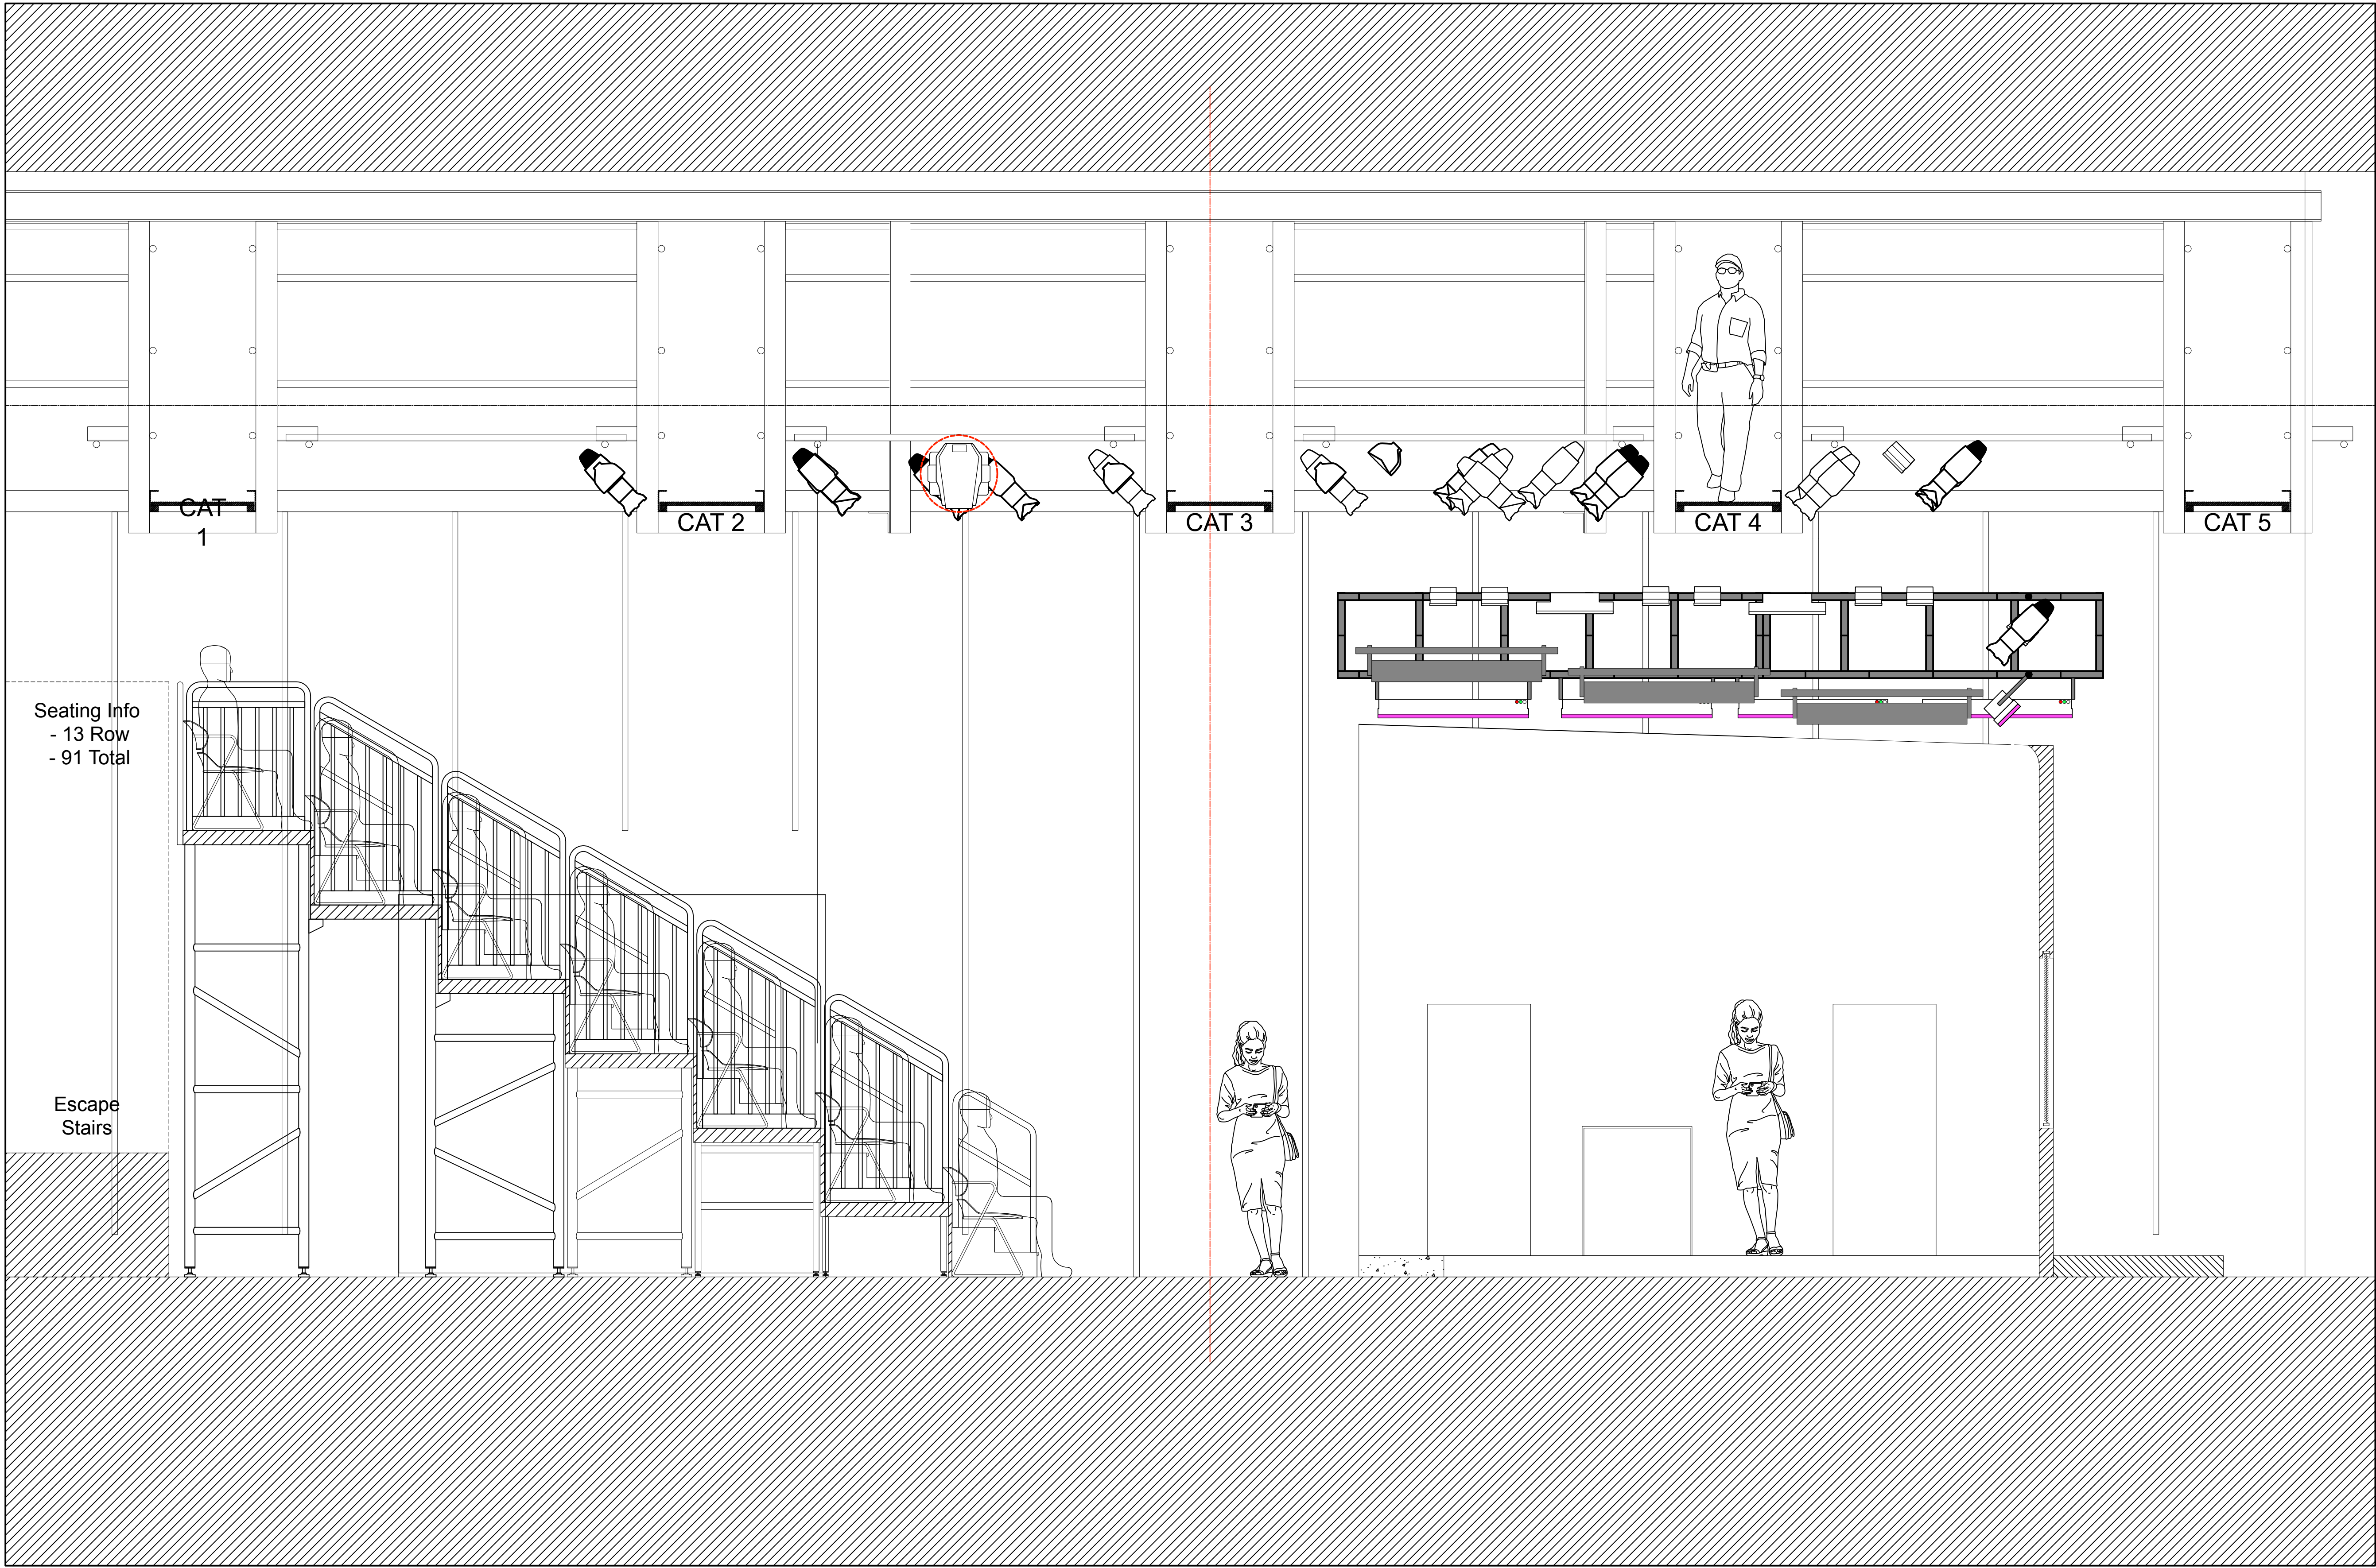

Symbol Key:

- ETC Source 4 14deg @575 W
- ETC Source 4 19deg @575 W
- ETC Source 4 26deg @575 W
- ETC Source 4 36deg @575 W
- ETC Source 4 50deg @575 W
- ETC Source 4 PAR MFL @575 W
- ETC Source 4 PAR WFL @575 W
- Hazebase Base Hazer Pro @1500 W
- Elation Level Q7 @127
- ETC Paletta 42 @432 W
- High End Systems SolaFrame 750 @562 W
- Cuepix Tri @0 W

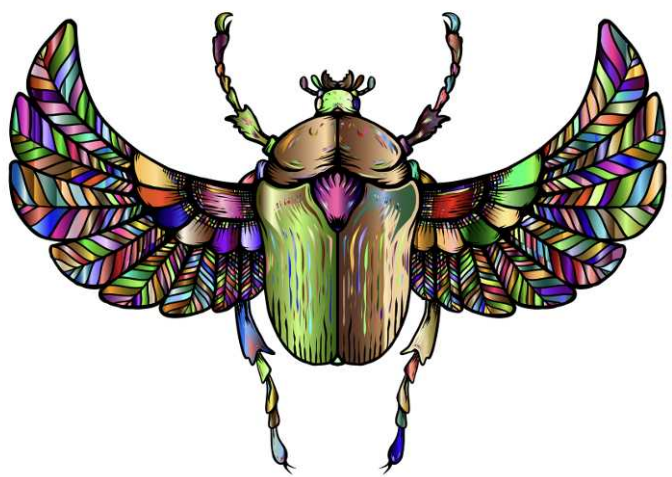

LEFT UNHEARD


HEALY THEATER AT DEPAUL THEATER SCHOOL
2400 N SHEFFIELD AVE CHICAGO, IL

DIRECTOR	DENISE SERNA
SCENIC DESIGNER	IZAAK KARY
LIGHTING DESIGNER	ADRIEN MATHIEU
STAGE MANAGEMENT	TESS DUNCAN
COSTUME DESIGNER	SPENCER HARRIGAN
TECHNICAL DIRECTOR	REID STADELMAN
WAM DESIGNER	CARISSA SETH
SOUND DESIGNER	MIA HOWARD

DATE: 3/30/25 SCALE: 1/4=1'0"


PLATE
3
OF 6

SECTION

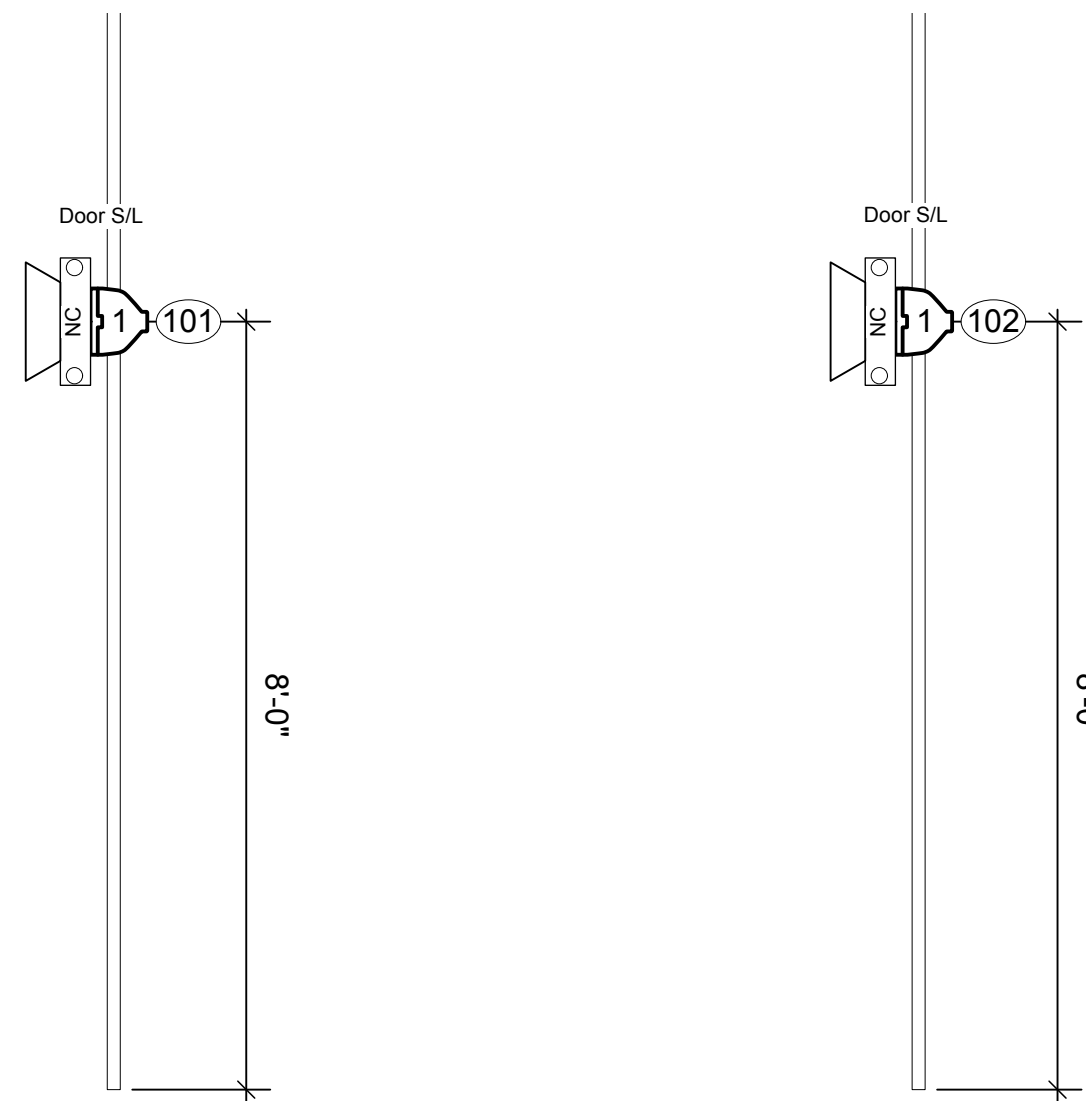

SL UNISTRUT #10

SR UNISTRUT #10

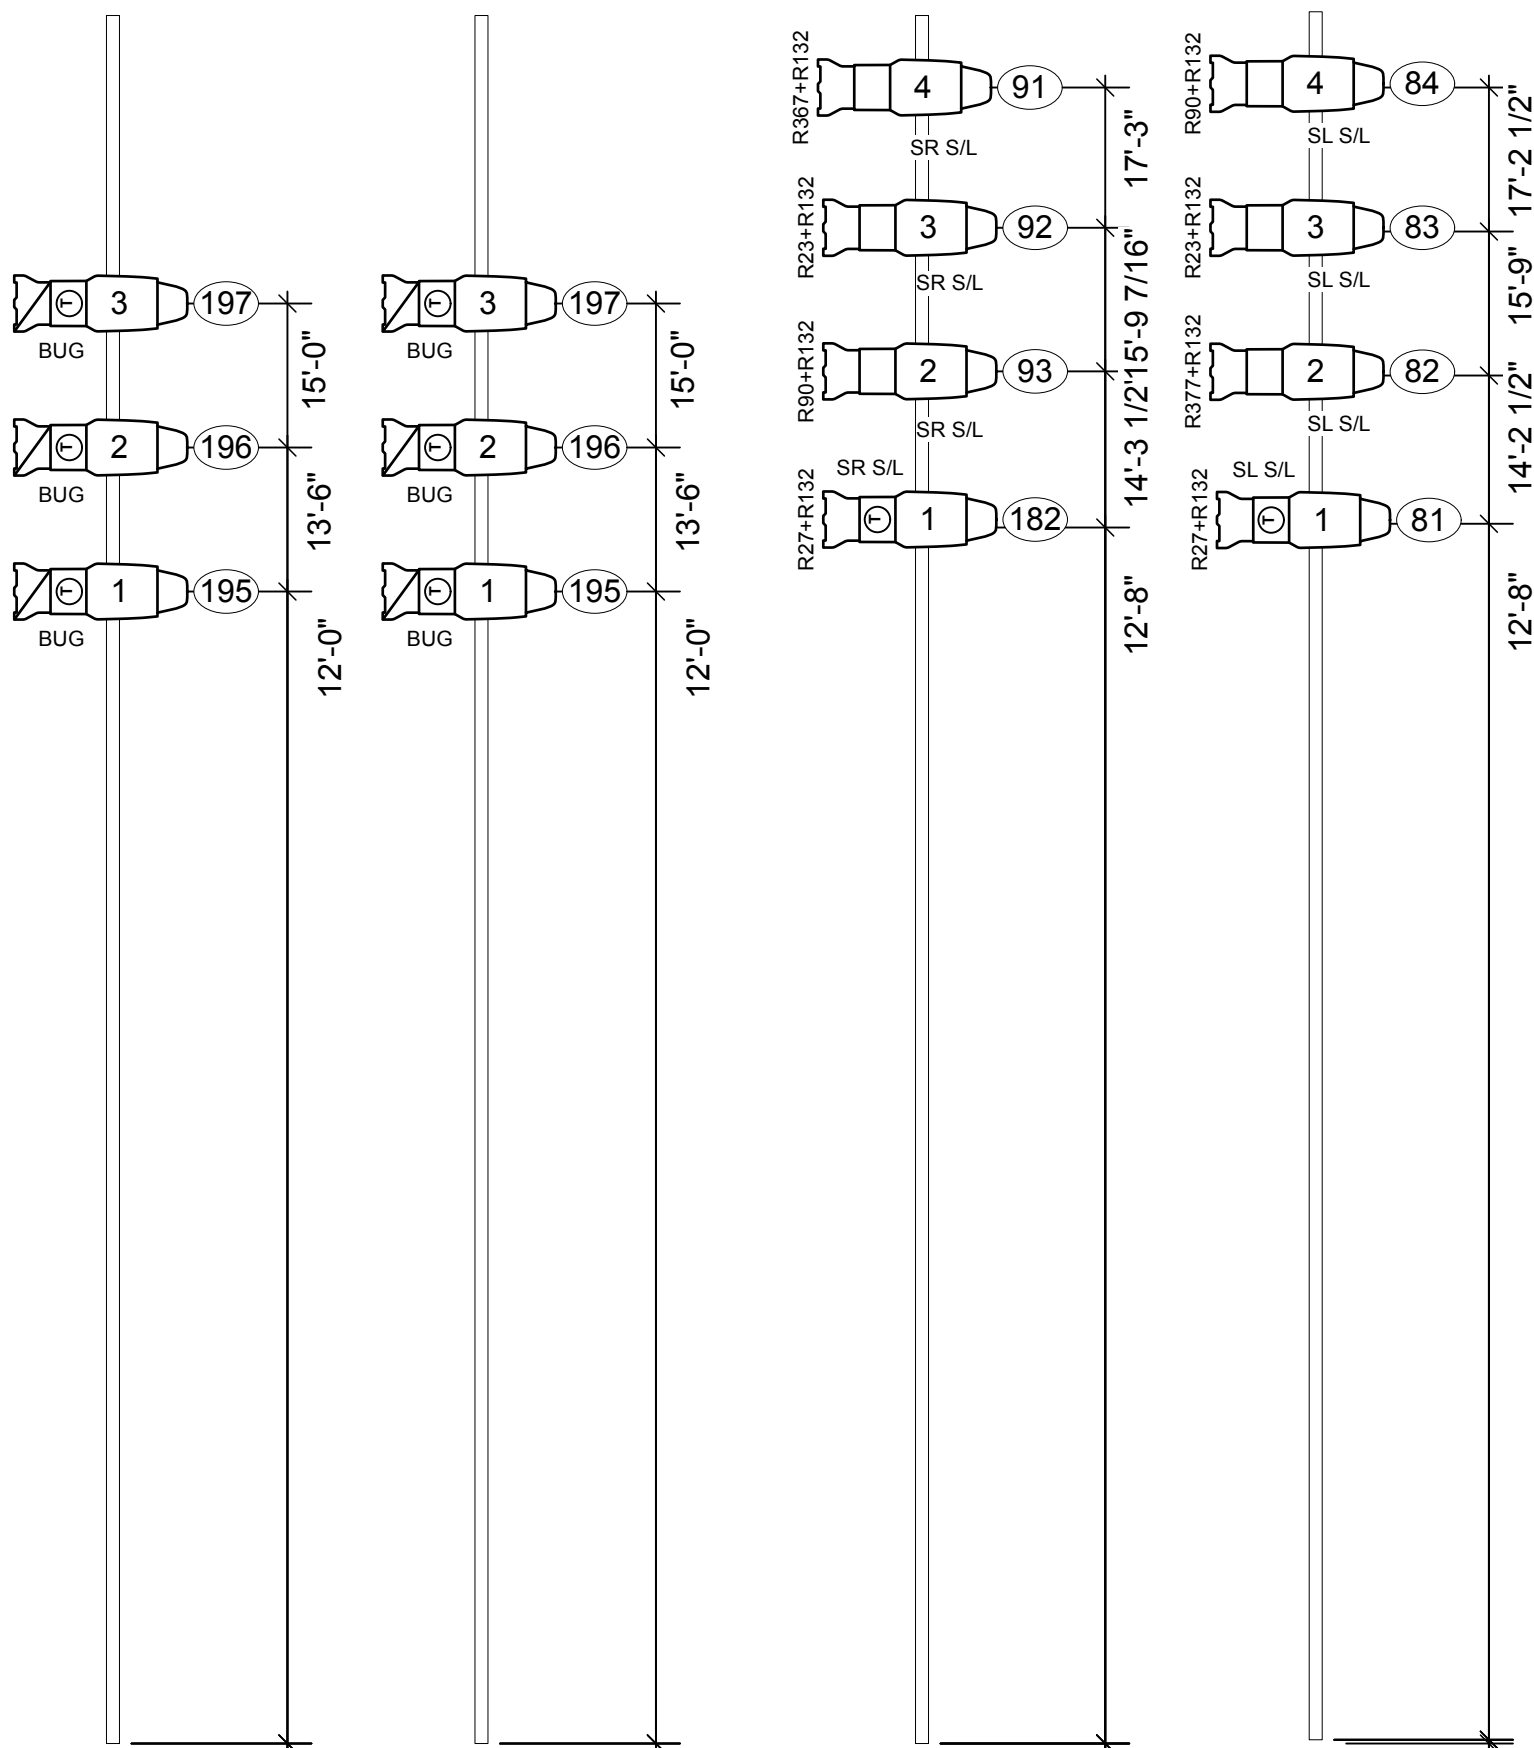

SL UNISTRUT #7


SR UNISTRUT #7

SL UNISTRUT #8


SR UNISTRUT #8

UNISTRUT


NOTE: UNISTRUT COUNTED DS TO US

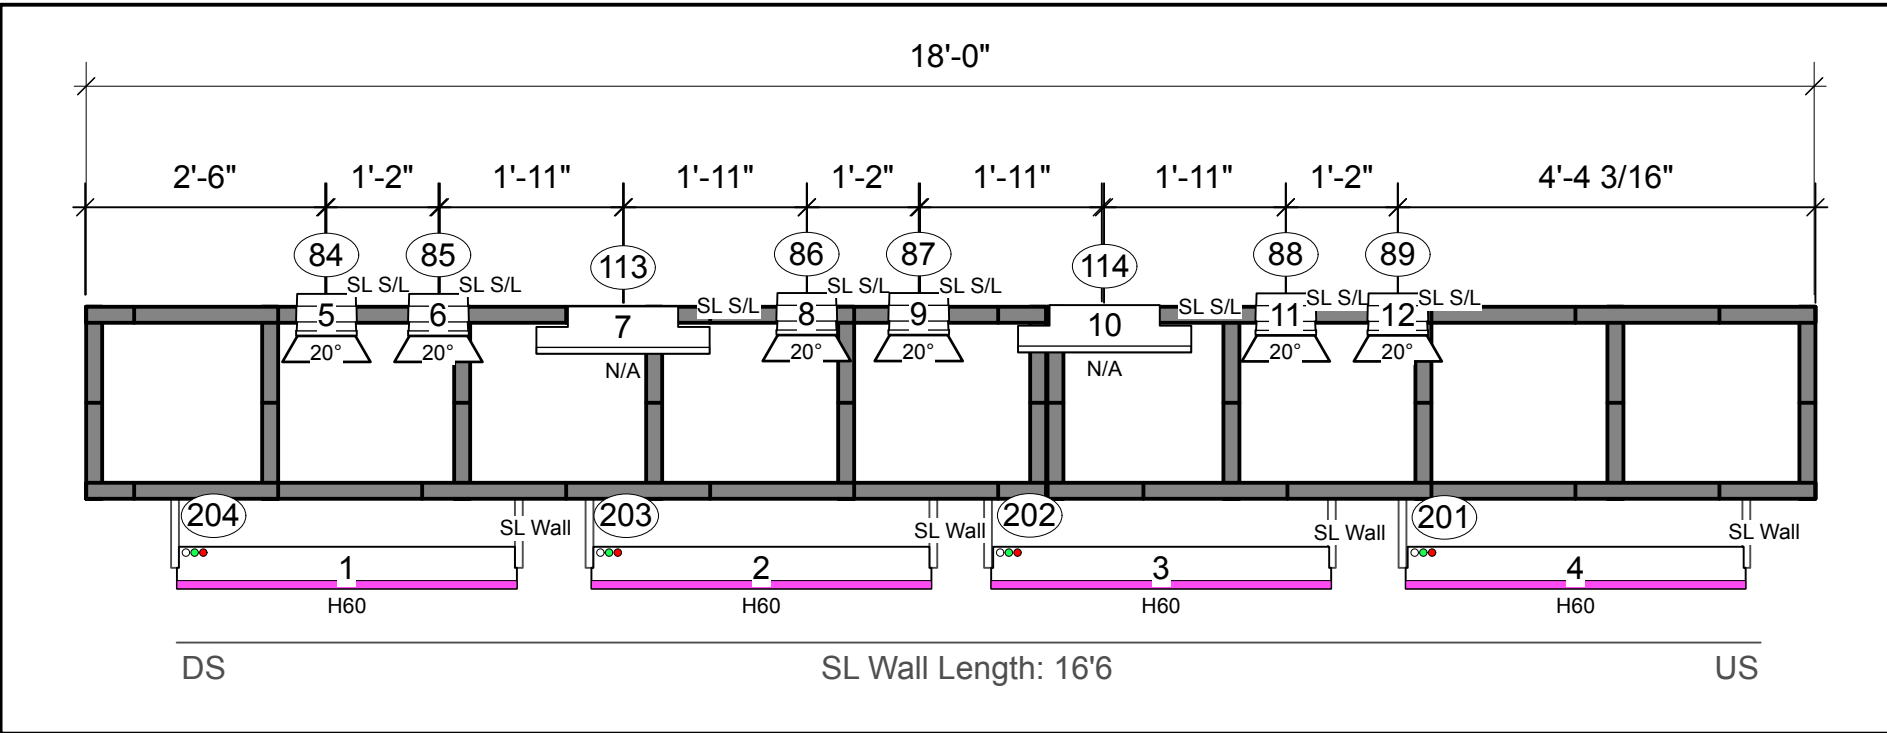


SL TRUSS
TRIM HIGHT: 14'0"/16'0"

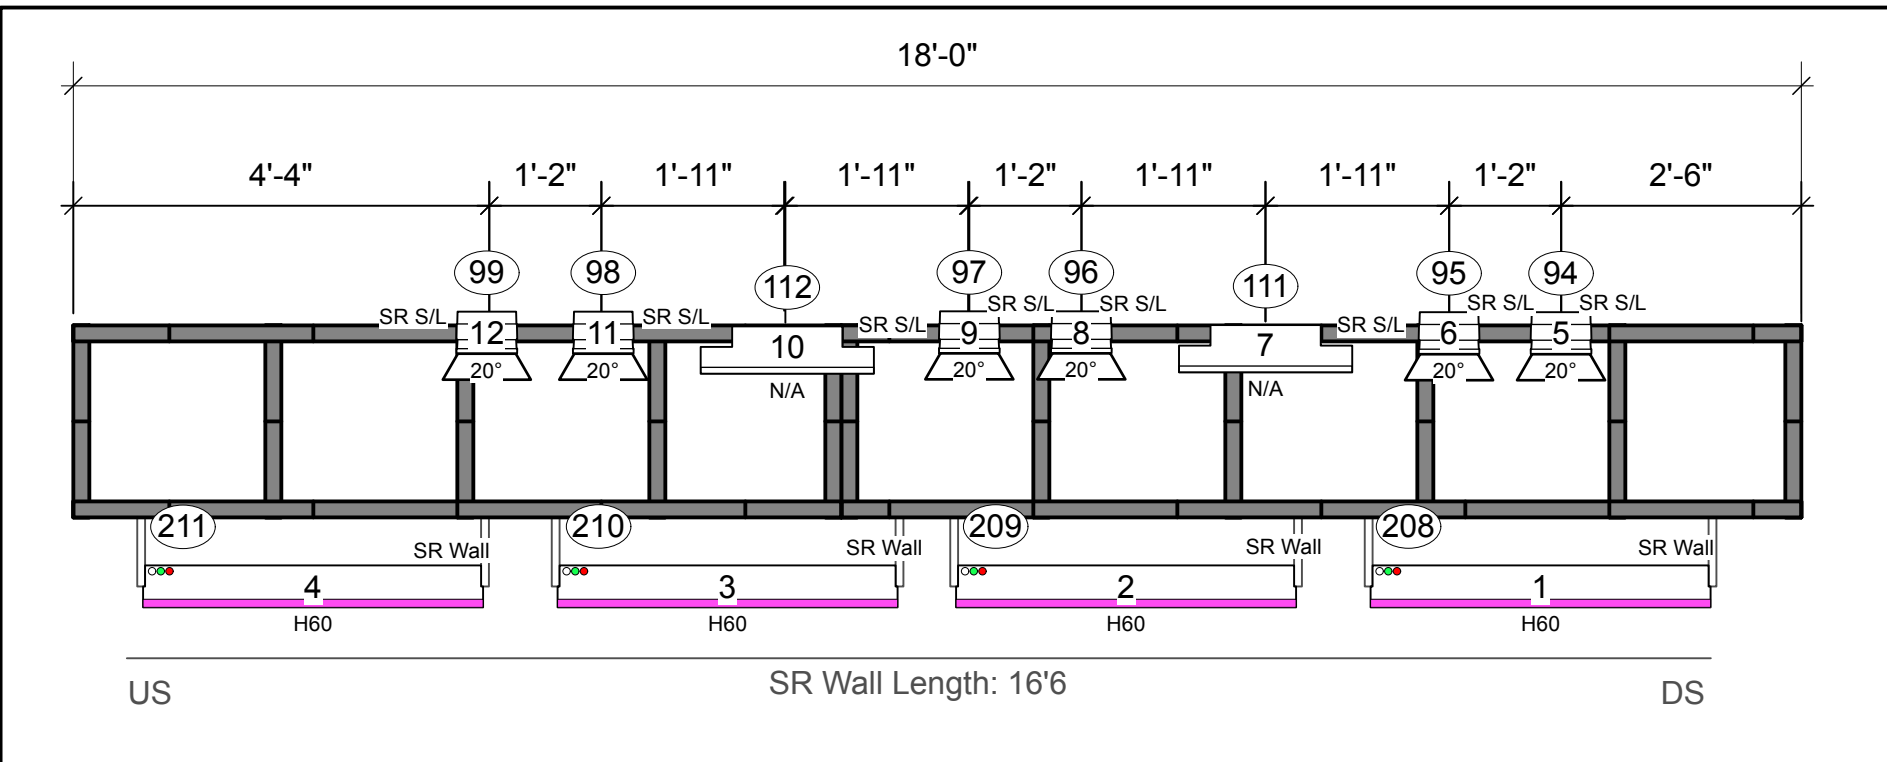


SR TRUSS
TRIM HIGHT: 14'0"/16'0"

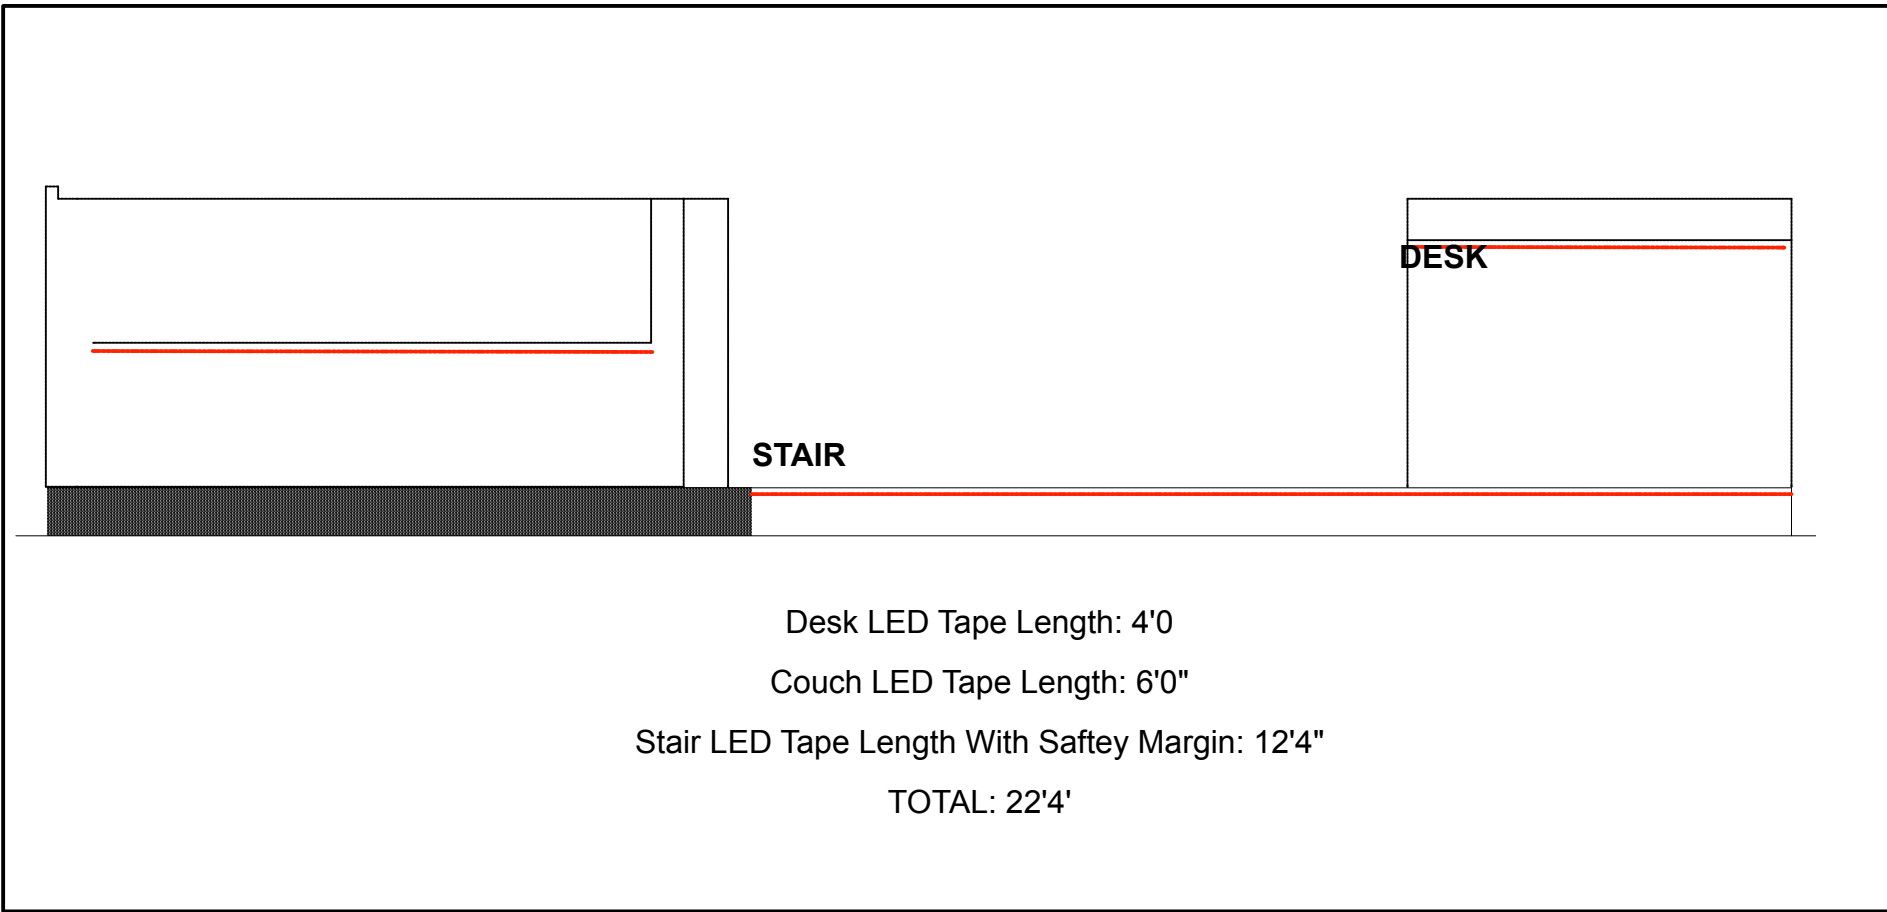


FURNITURE LED

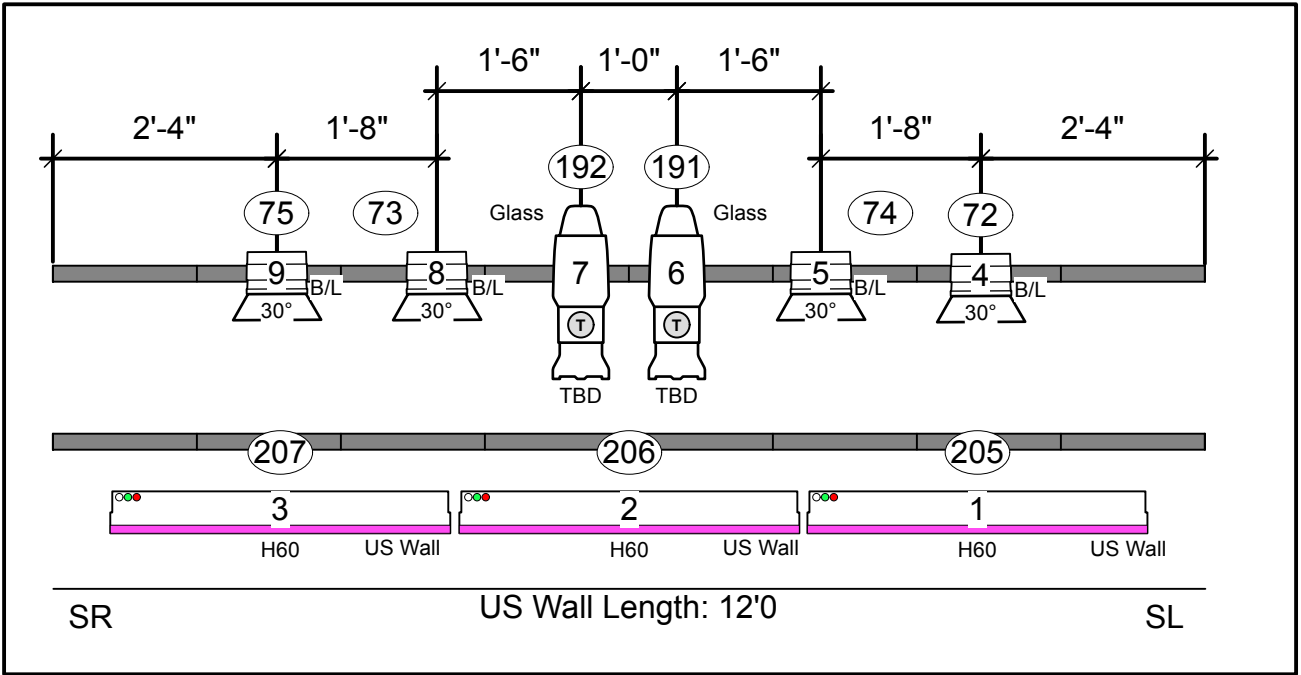

US PIPES
TRIM HIGHT: 14'0"/16'0"

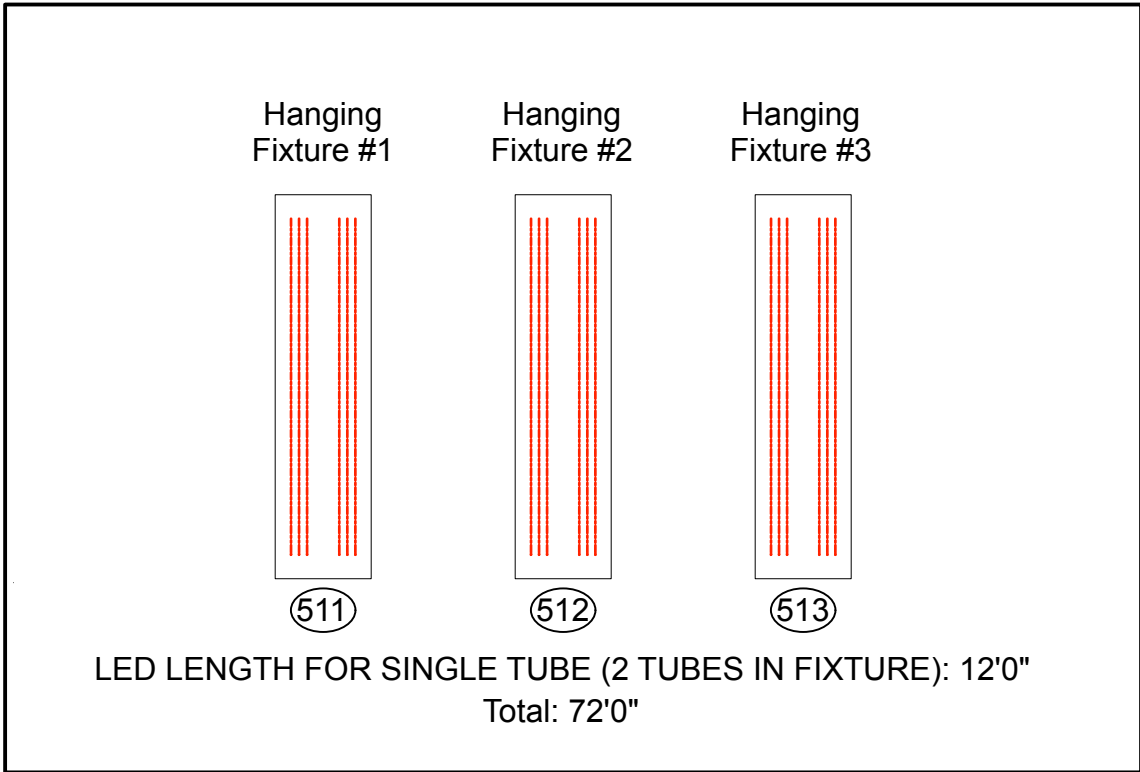


HANGING FIXTURE LED
#1 TRIM HIGHT: 13'0"
#2 TRIM HIGHT: 13'6"
#3 TRIM HIGHT: 14'0"

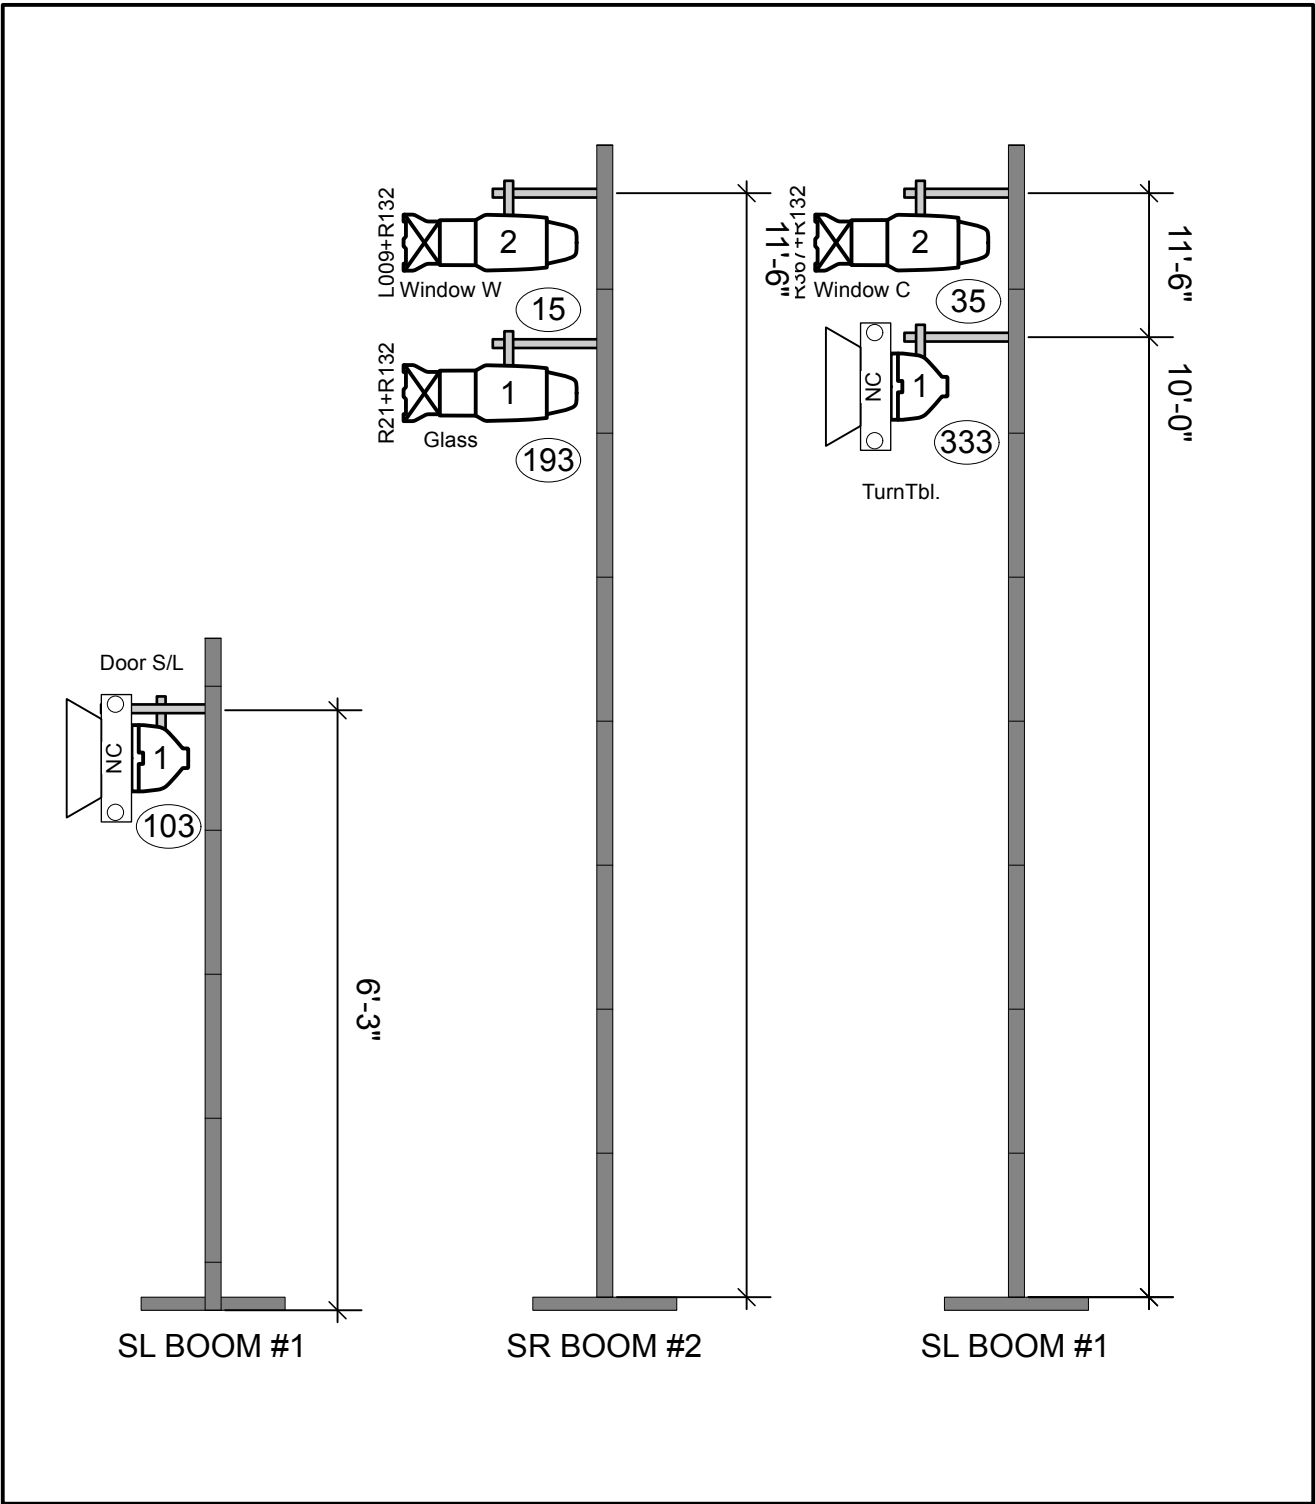

BOOMS

Symbol Key:

- ETC Source 4 14deg @575 W
- ETC Source 4 19deg @575 W
- ETC Source 4 26deg @575 W
- ETC Source 4 36deg @575 W
- ETC Source 4 50deg @575 W
- ETC Source 4 PAR MFL @575 W
- ETC Source 4 PAR WFL @575 W
- Hazebase Base Hazer Pro @1500 W
- Elation Level Q7 @127
- ETC Paletta 42 @432 W
- High End Systems SolaFrame 750 @562 W
- Cuepix Tri @0 W

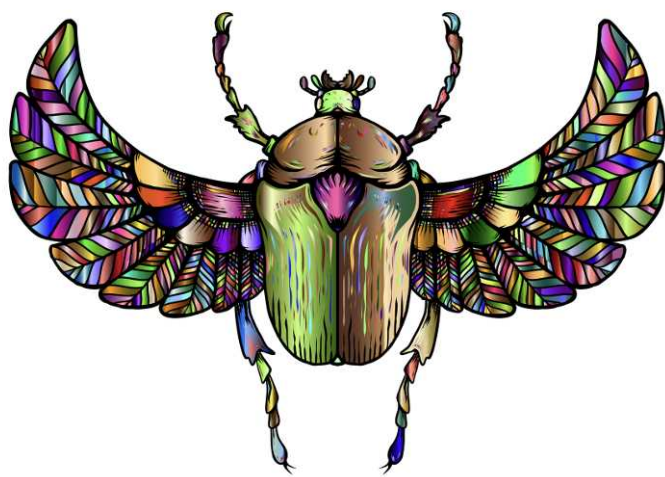

LEFT UNHEARD

HEALY THEATER AT DEPAUL THEATER SCHOOL
2400 N SHEFFIELD AVE CHICAGO, IL

DIRECTOR	DENISE SERNA
SCENIC DESIGNER	IZAAK KARY
LIGHTING DESIGNER	ADRIEN MATHIEU
STAGE MANAGEMENT	TESS DUNCAN
COSTUME DESIGNER	SPENCER HARRIGAN
TECHNICAL DIRECTOR	REID STADELMAN
WAM DESIGNER	CARISSA SETH
SOUND DESIGNER	MIA HOWARD


DATE: 3/30/25 SCALE: 1/4=1'0"

PLATE

4


OF 6

MISC. POSITIONS

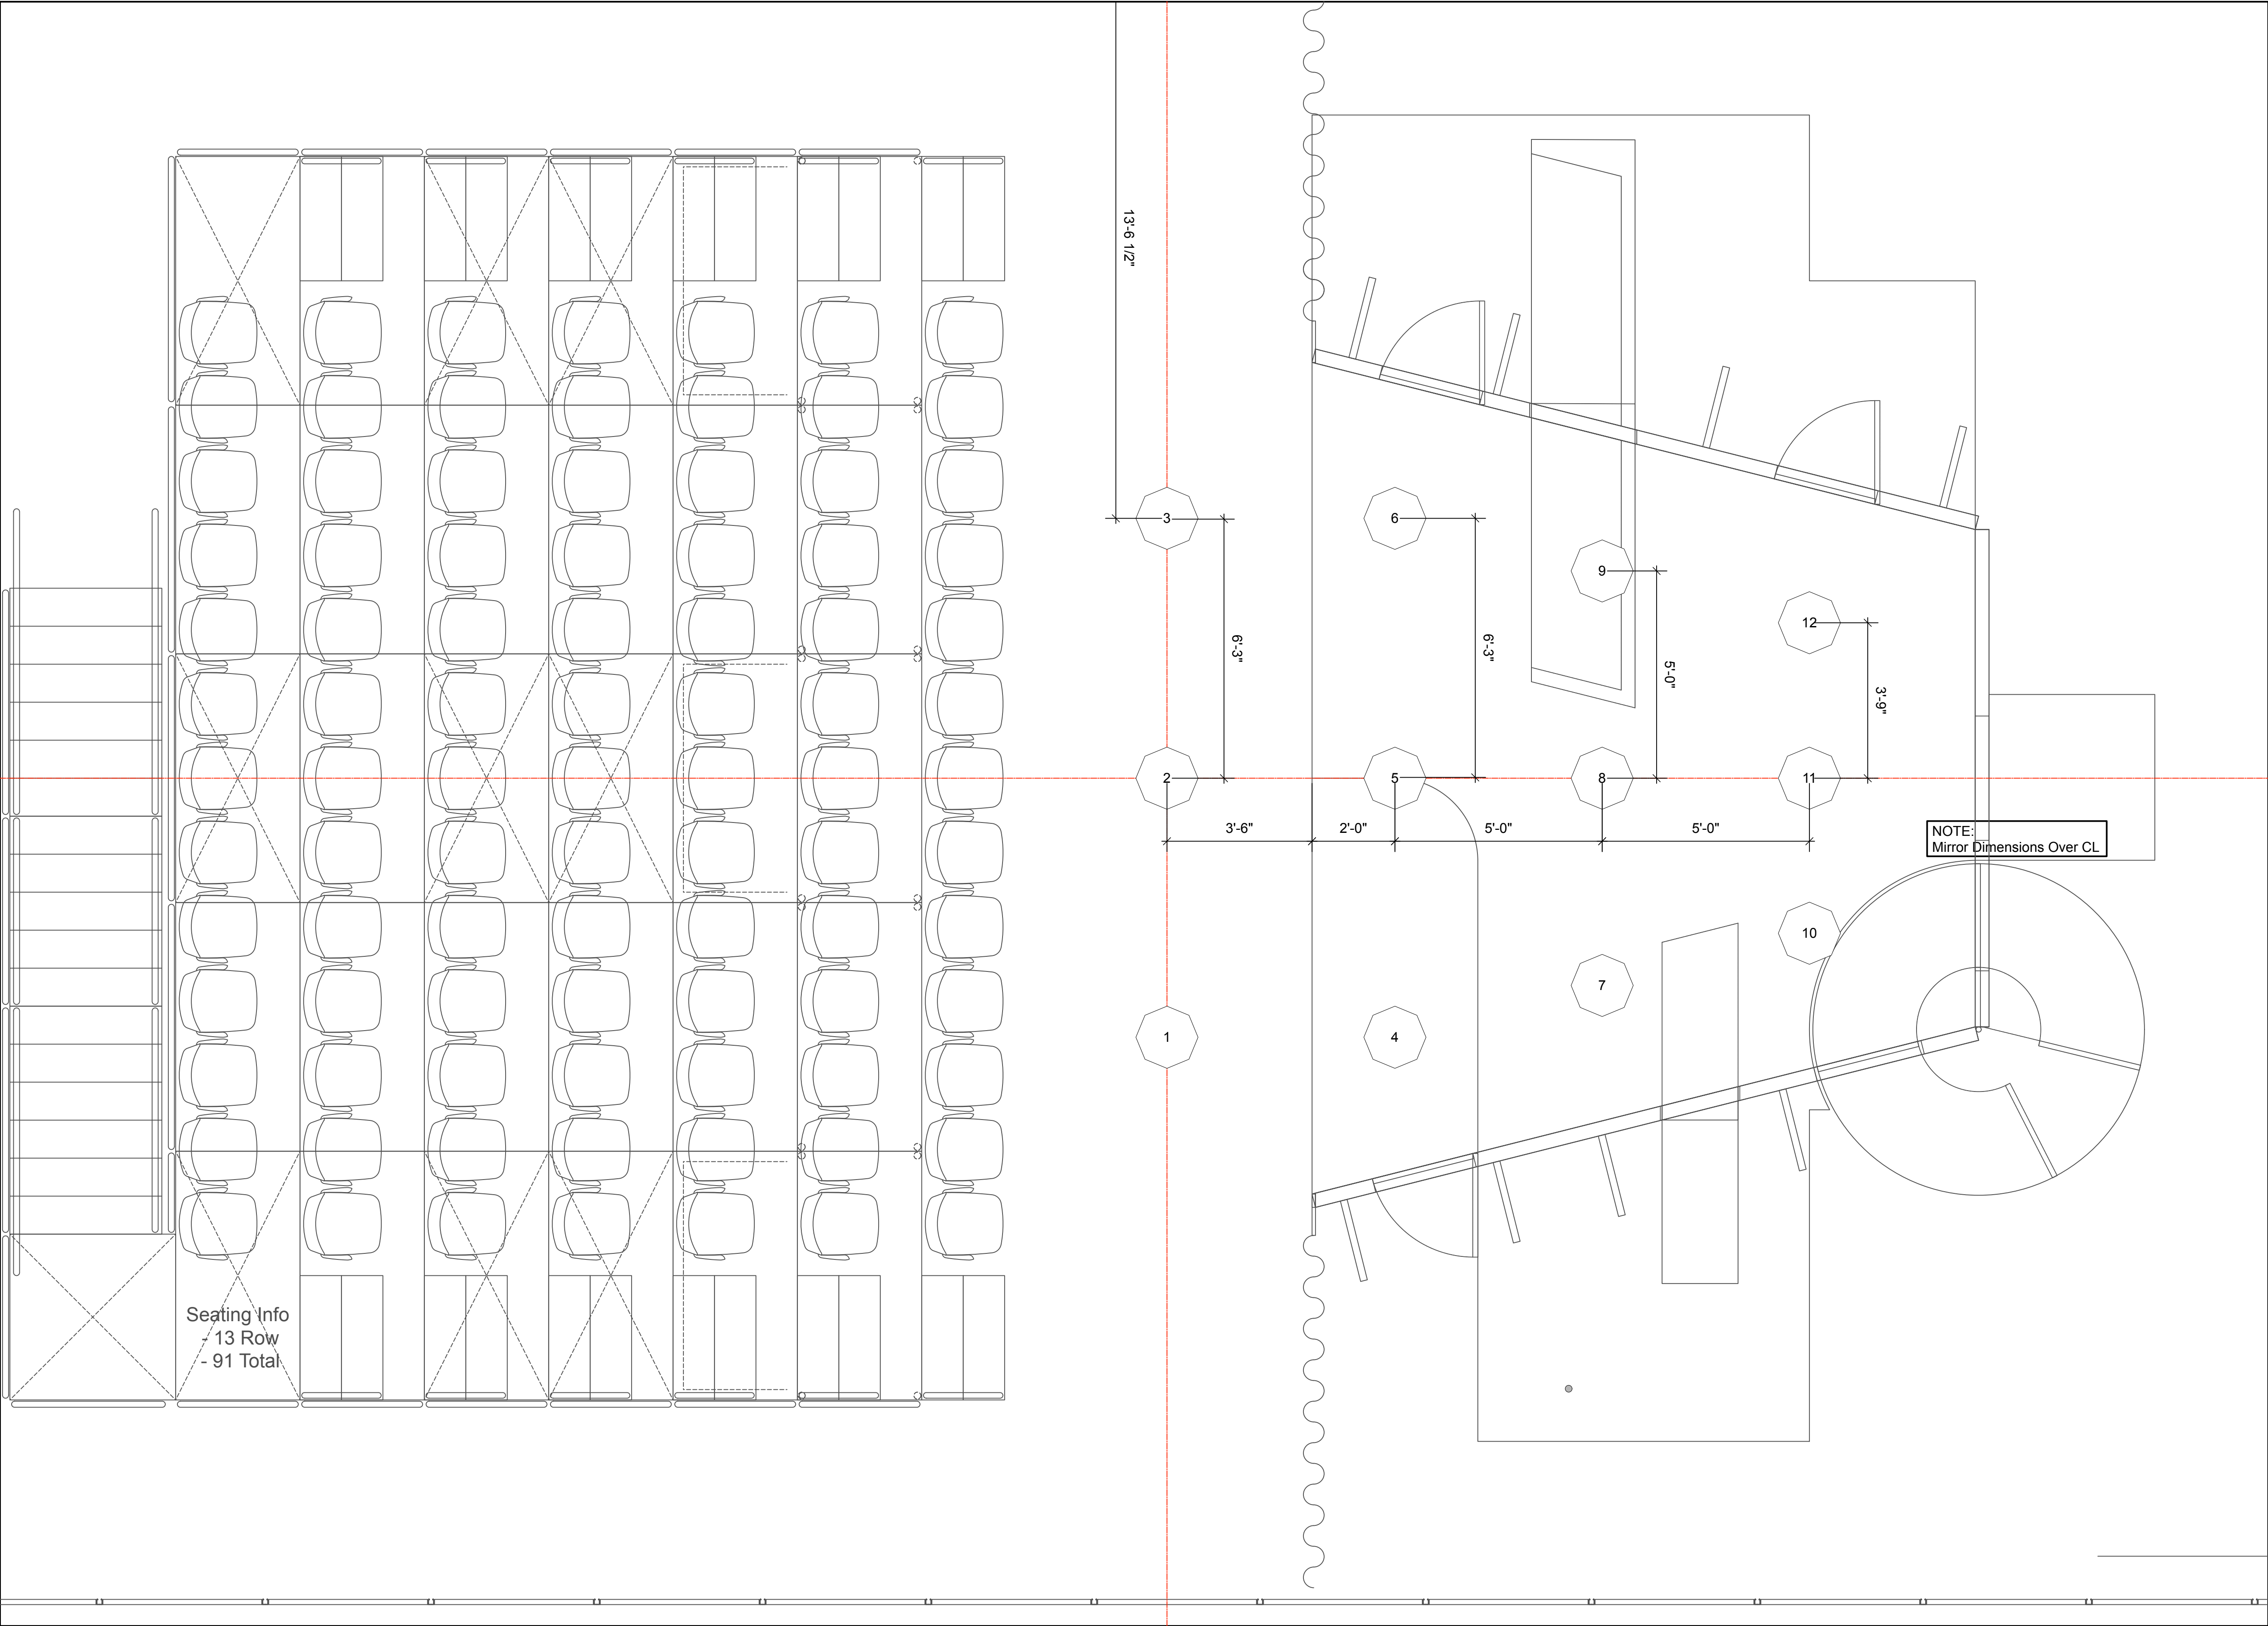

Symbol Key:

- ETC Source 4 14deg @575 W
- ETC Source 4 19deg @575 W
- ETC Source 4 26deg @575 W
- ETC Source 4 36deg @575 W
- ETC Source 4 50deg @575 W
- ETC Source 4 PAR MFL @575 W
- ETC Source 4 PAR WFL @575 W
- Hazebase Base Hazer Pro @1500 W
- Elation Level Q7 @127
- ETC Paletta 42 @432 W
- High End Systems SolaFrame 750 @562 W
- Cuepix Tri @0 W

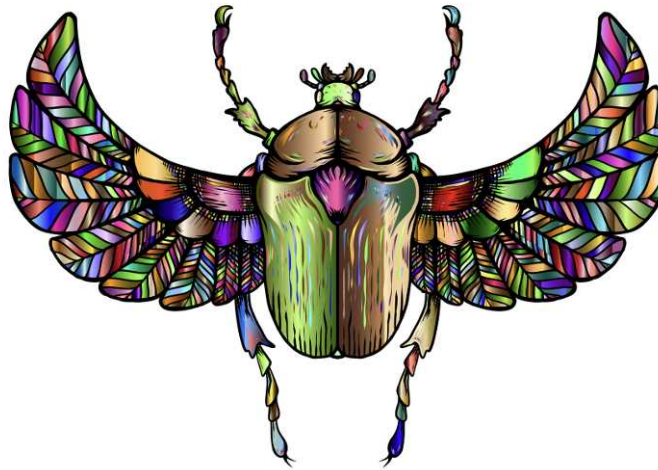

LEFT UNHEARD

HEALY THEATER AT DEPAUL THEATER SCHOOL
2400 N SHEFFIELD AVE CHICAGO, IL

DIRECTOR	DENISE SERNA
SCENIC DESIGNER	IZAAK KARY
LIGHTING DESIGNER	ADRIEN MATHIEU
STAGE MANAGEMENT	TESS DUNCAN
COSTUME DESIGNER	SPENCER HARRIGAN
TECHNICAL DIRECTOR	REID STADELMAN
WAM DESIGNER	CARISSA SETH
SOUND DESIGNER	MIA HOWARD

DATE: 3/30/25


SCALE: 1/4=1'0"

PLATE

5


OF 6

AREAS

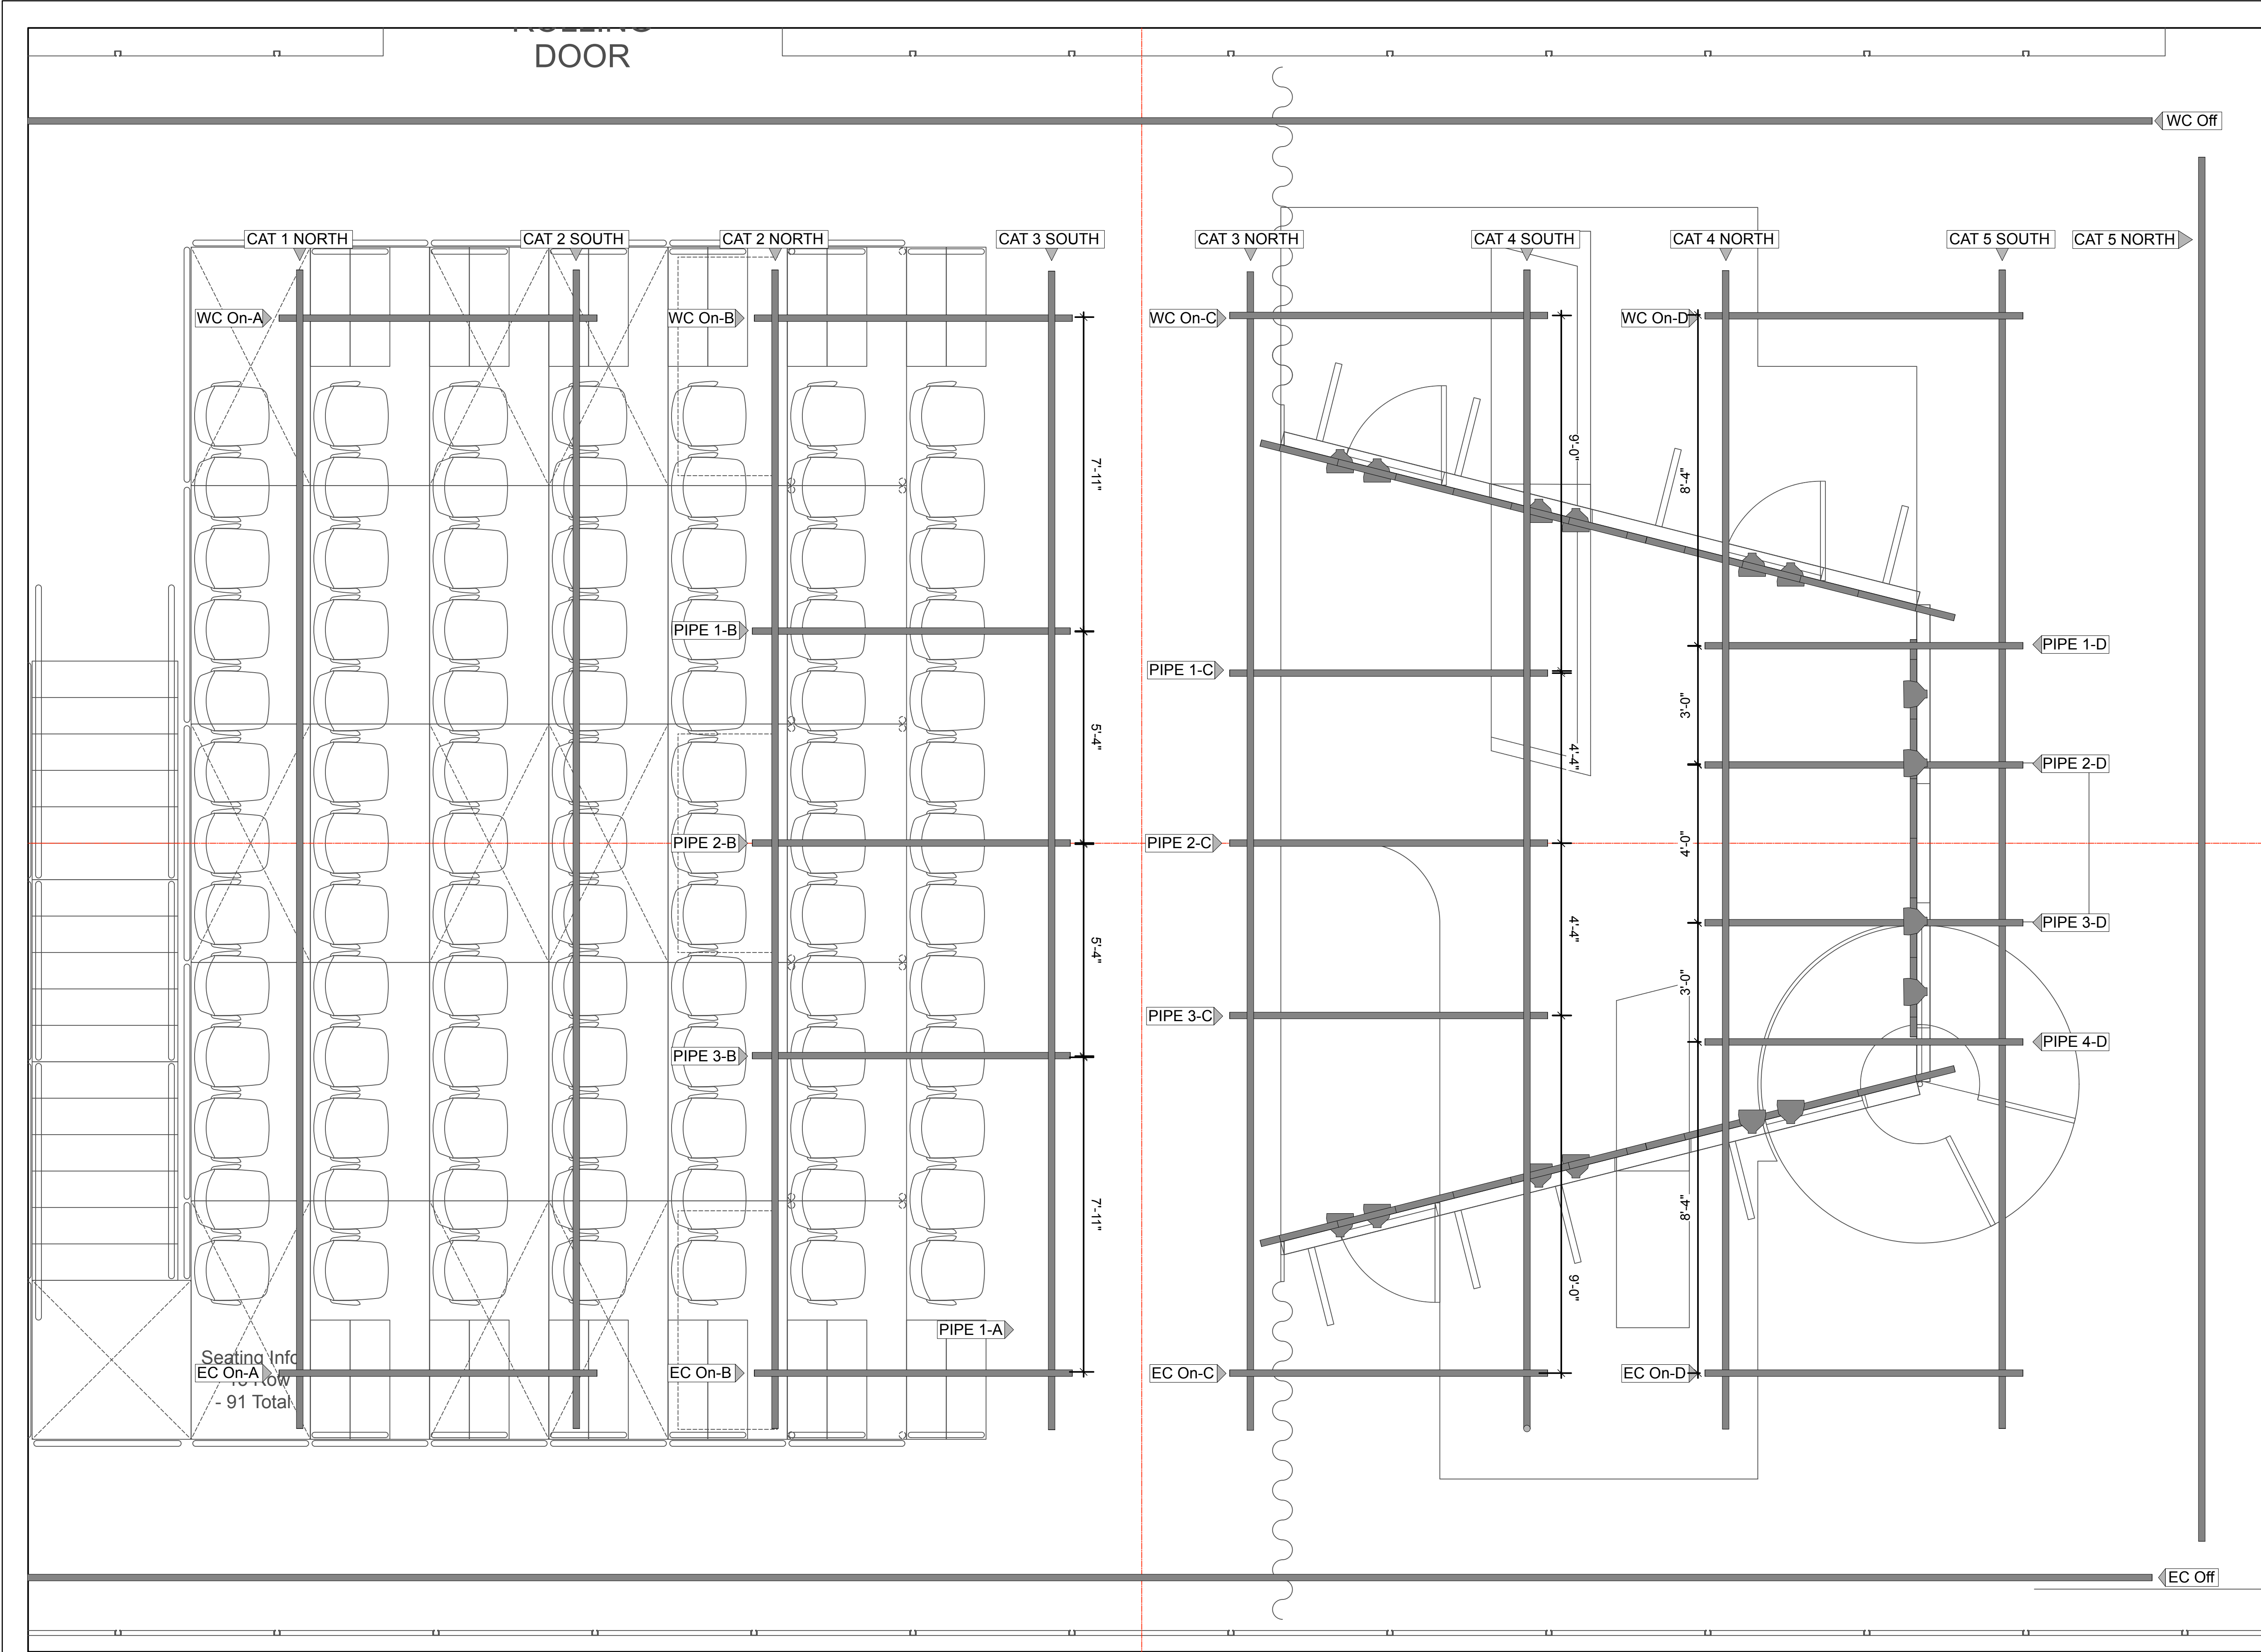

Symbol Key:

- ETC Source 4 14deg @575 W
- ETC Source 4 19deg @575 W
- ETC Source 4 26deg @575 W
- ETC Source 4 36deg @575 W
- ETC Source 4 50deg @575 W
- ETC Source 4 PAR MFL @575 W
- ETC Source 4 PAR WFL @575 W
- Hazebase Base Hazer Pro @1500 W
- Elation Level Q7 @127
- ETC Paletta 42 @432 W
- High End Systems SolaFrame 750 @562 W
- Cuepix Tri @0 W

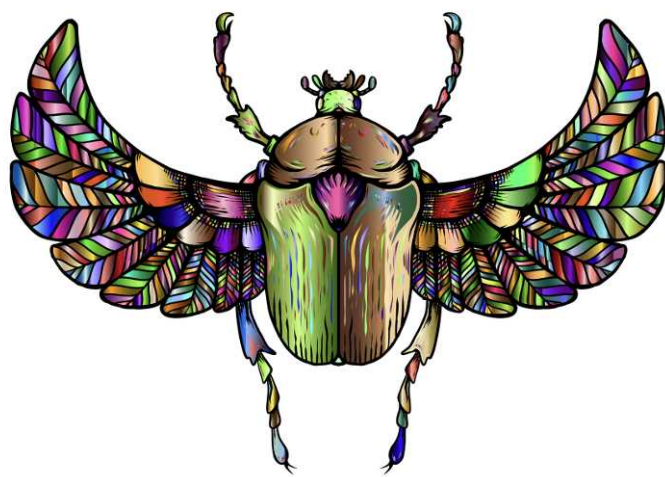

LEFT UNHEARD

HEALY THEATER AT DEPAUL THEATER SCHOOL
2400 N SHEFFIELD AVE CHICAGO, IL

DIRECTOR	DENISE SERNA
SCENIC DESIGNER	IZAAK KARY
LIGHTING DESIGNER	ADRIEN MATHIEU
STAGE MANAGEMENT	TESS DUNCAN
COSTUME DESIGNER	SPENCER HARRIGAN
TECHNICAL DIRECTOR	REID STADELMAN
WAM DESIGNER	CARISSA SETH
SOUND DESIGNER	MIA HOWARD

DATE: 3/30/25 SCALE: 1/4=1'0"

PLATE

6

OF 6

PIPE LABLES + DIMENSIONS